


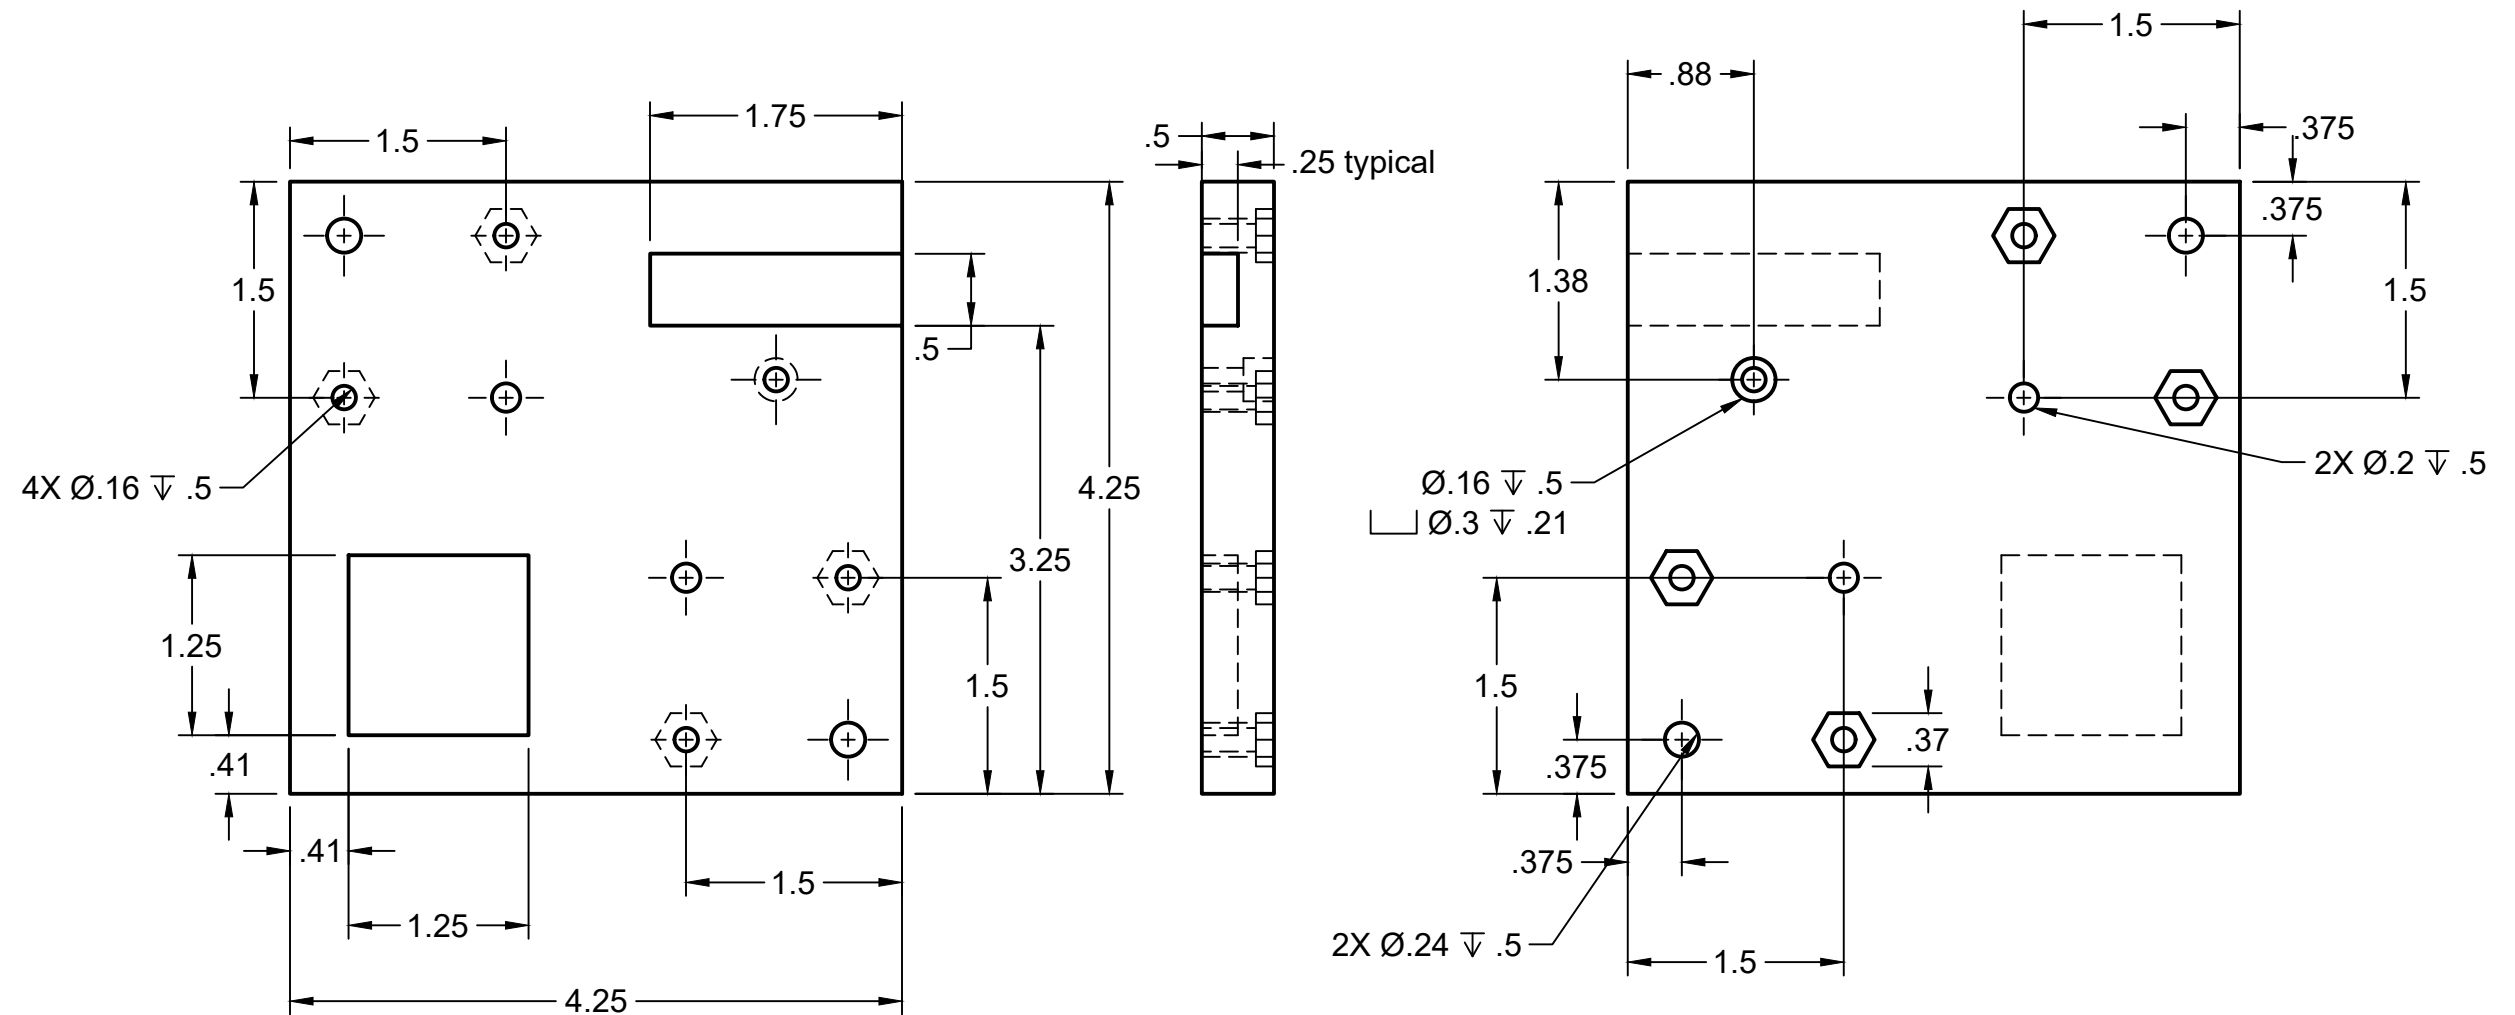

PROJECT			
QHS/PLTW - IED Block C			
TITLE			
Baseplate			
SIZE	CODE	DWG NO	REV
B			
SCALE .75	WEIGHT		SHEET 1/1